


Выходы для исполнительных устройств

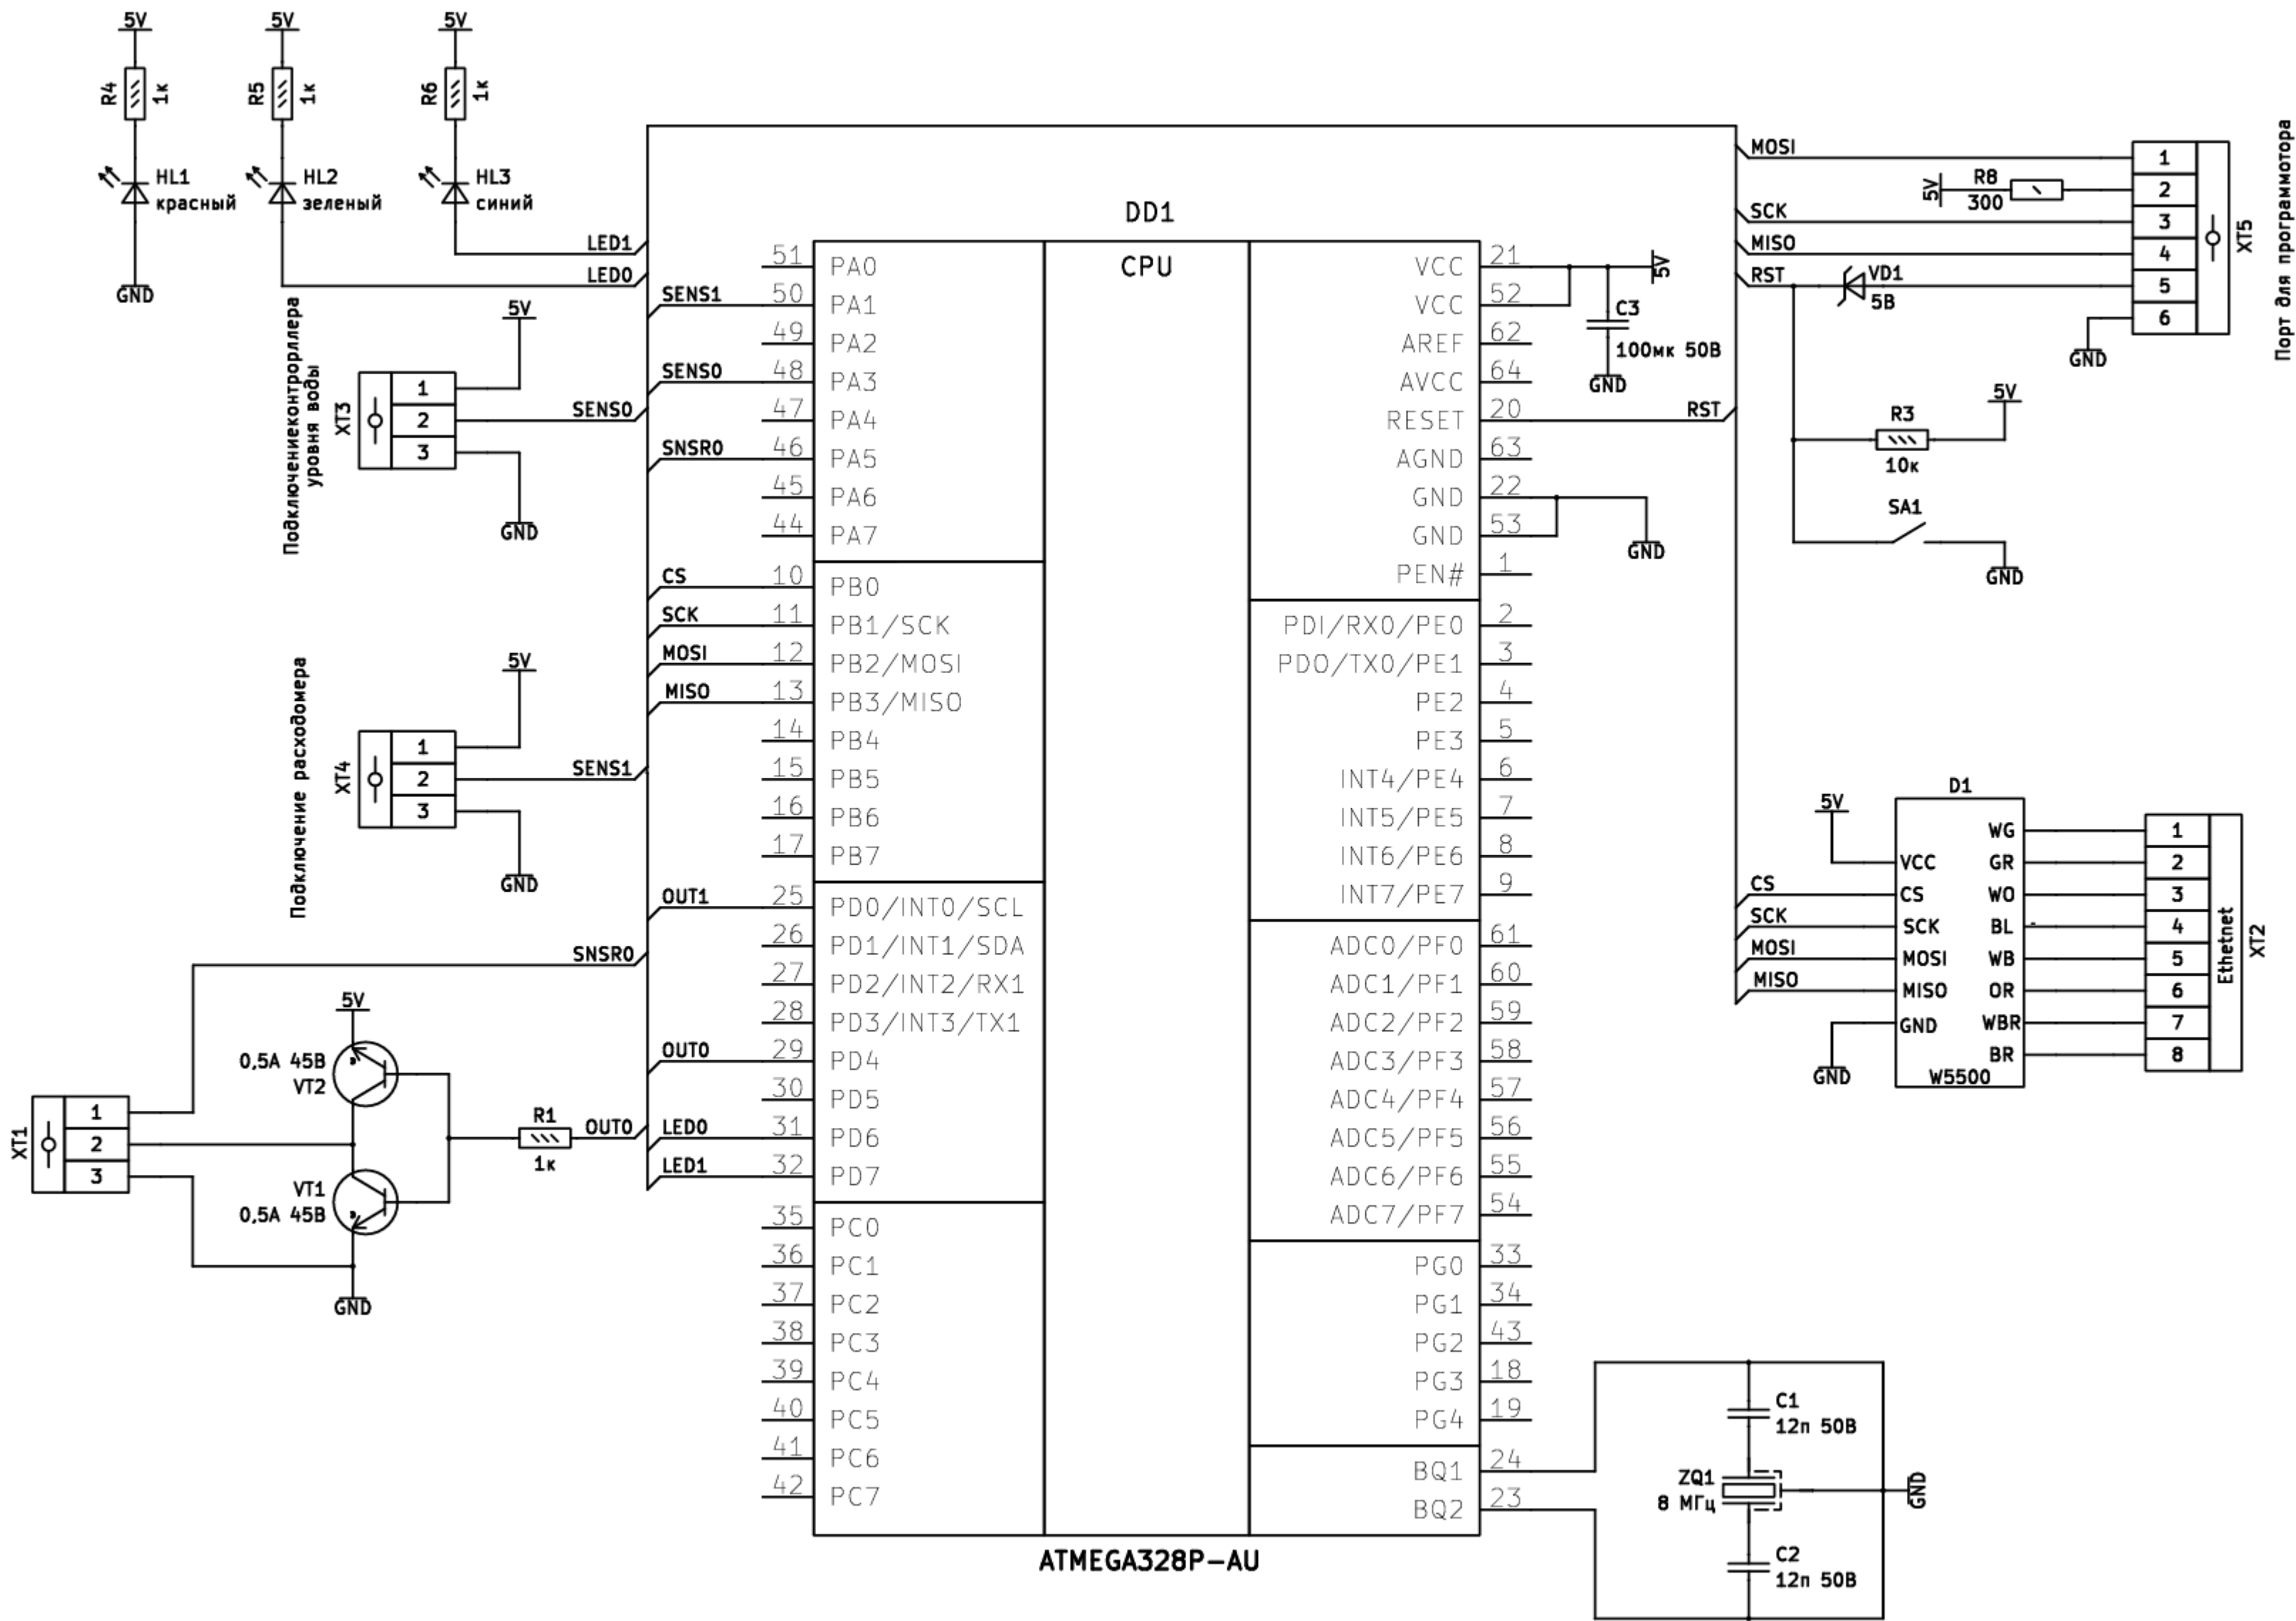

Порт для прошивки

Ethernet

Изм.	Лист	№ докум.	Подп.	Дата	Устройство для управления насосом для поддержания заданного уровня воды и передачи суточного расхода на заданный IP-адрес. Схема электрическая принципиальная	Лит.	Масса	Мощность
Разраб.	Буденов						-	-
Проб.	Бородин					Лист	Листов	1
Т.контр.						МГТУ им. Н.Э. Баумана группа ПС-82		
Н.контр.					Копировал	Формат А2		
Утв.								