
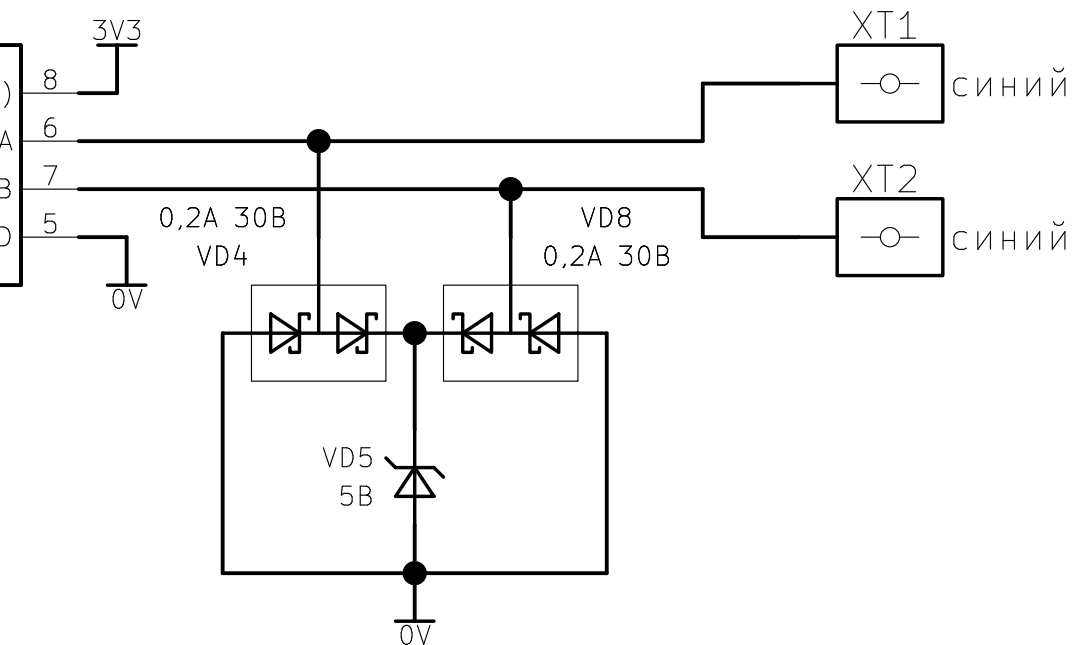
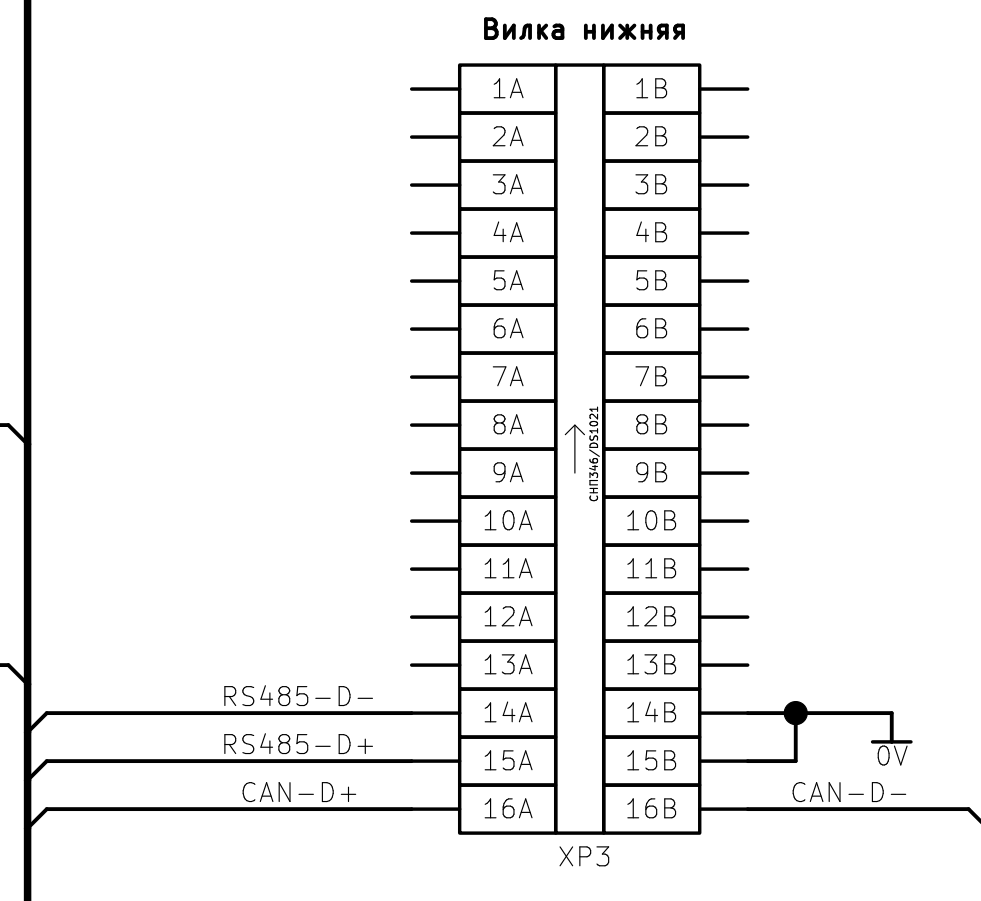
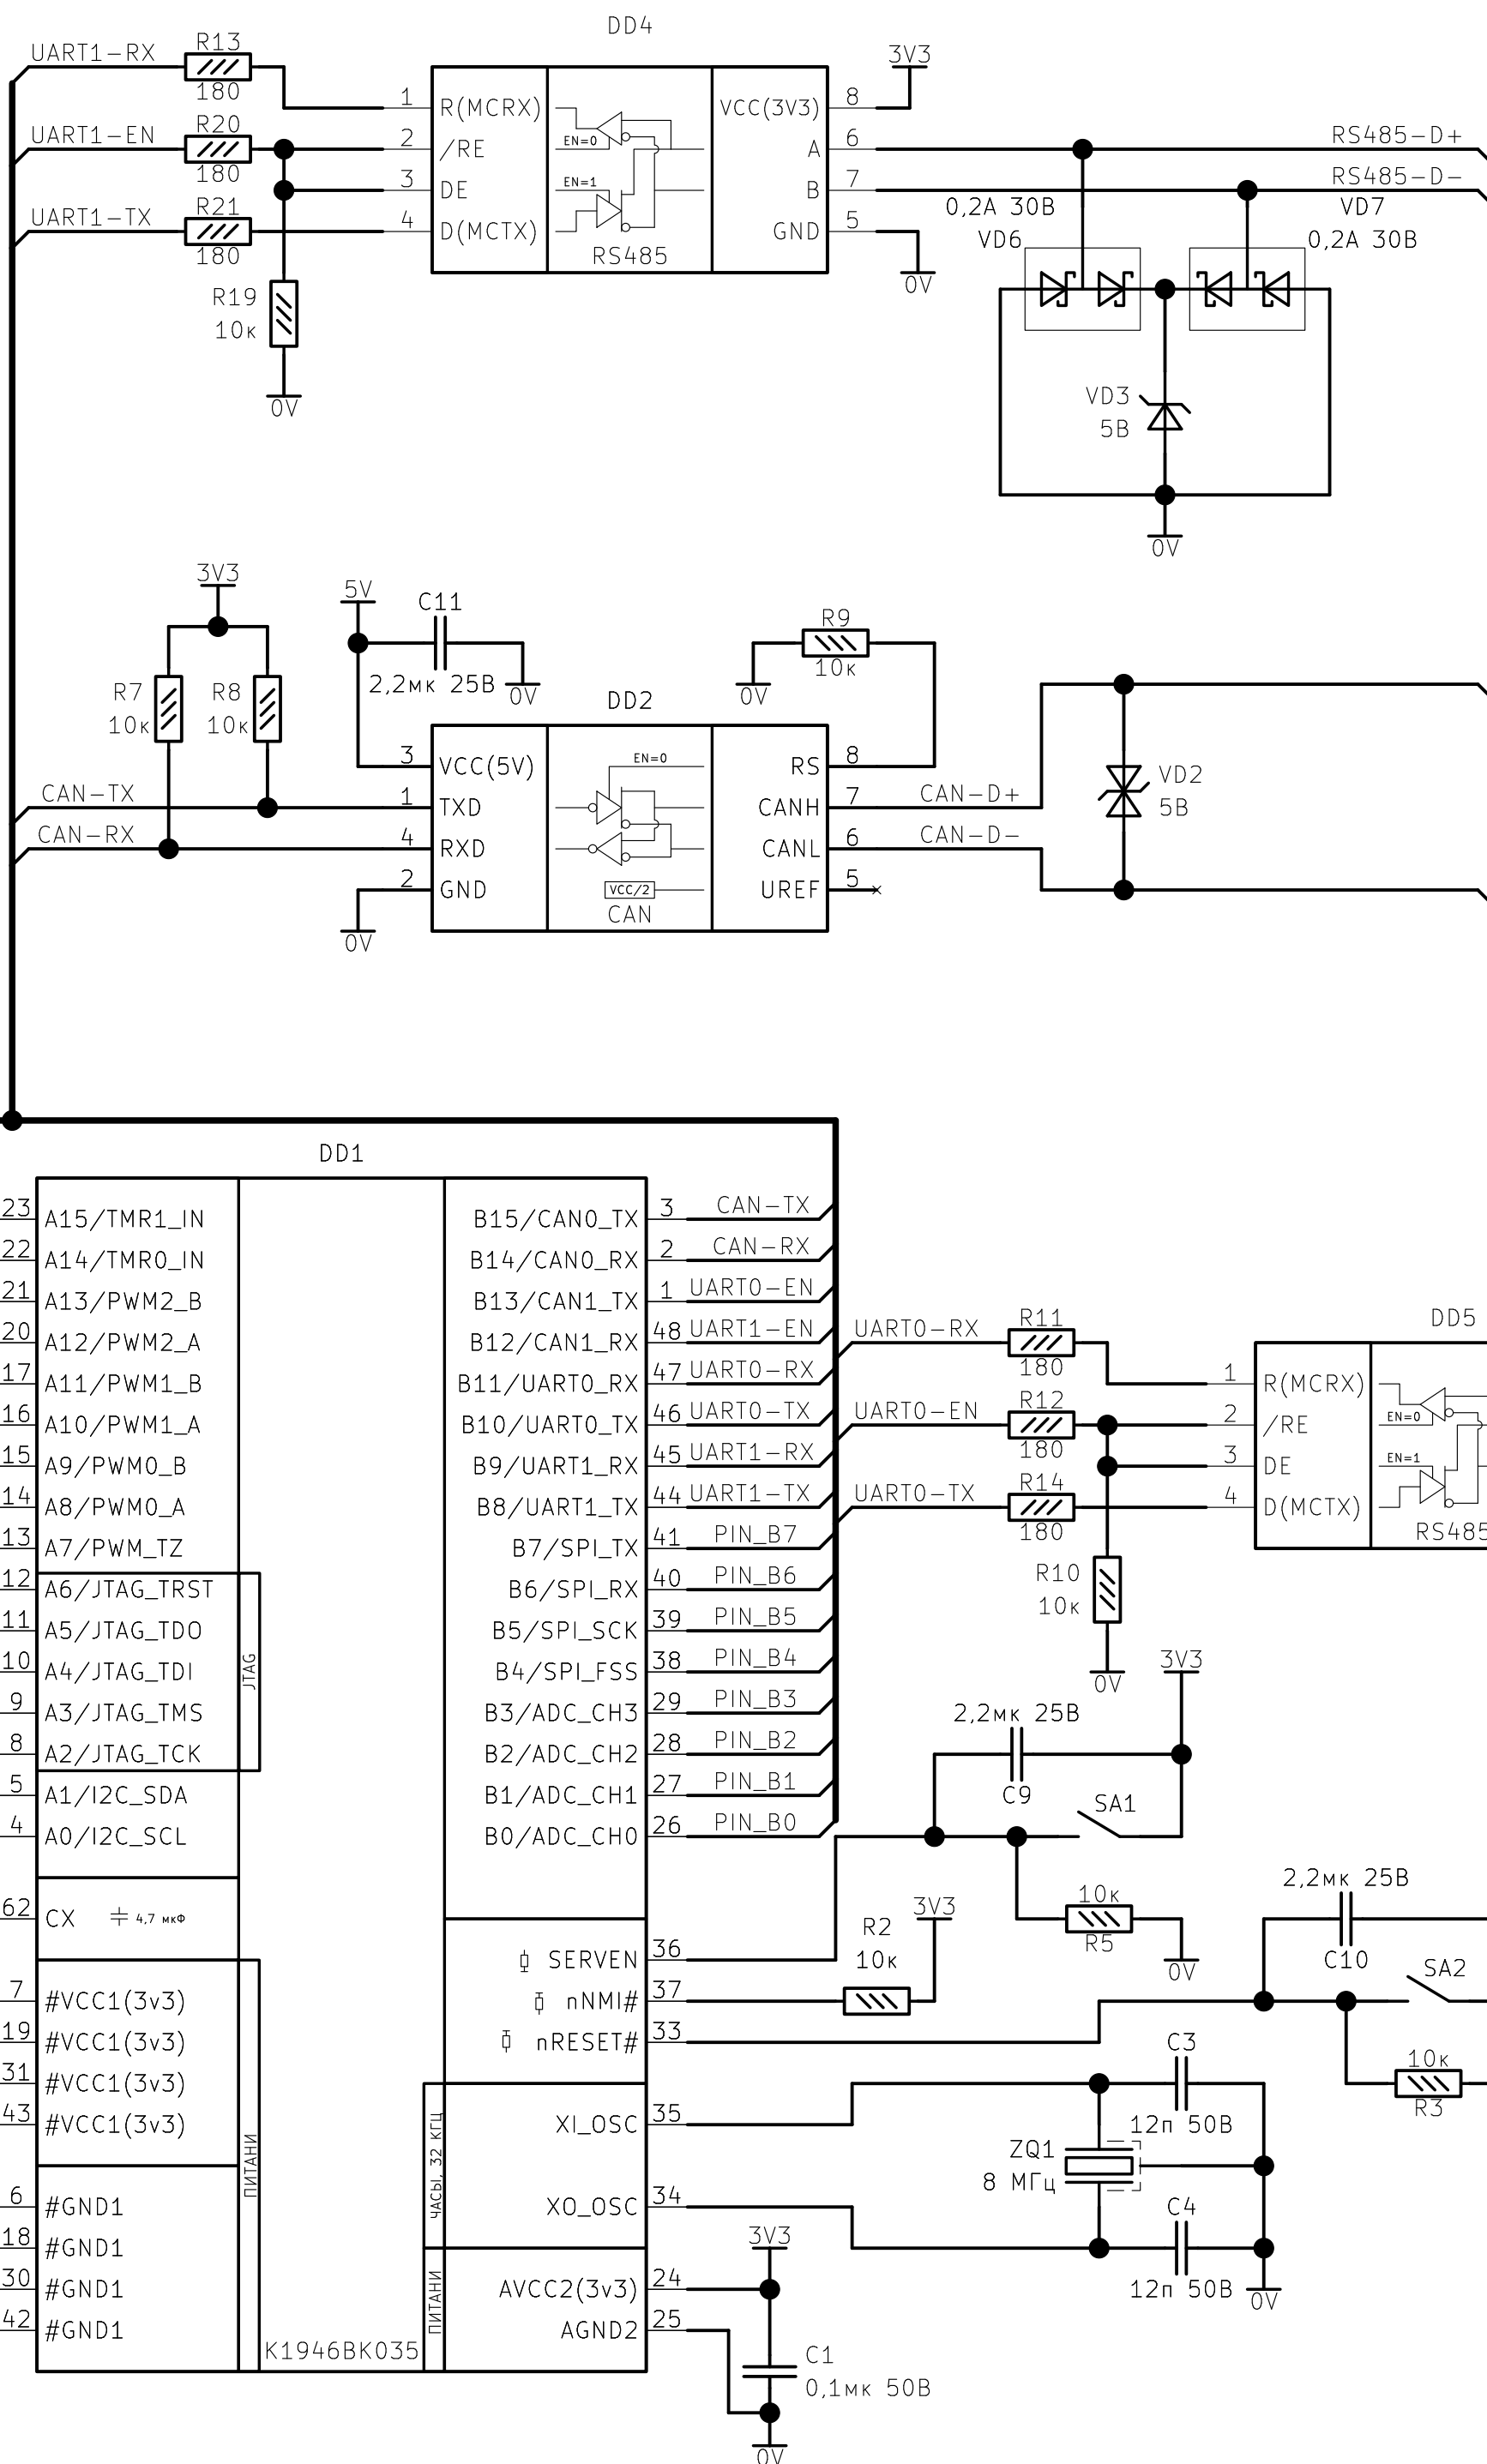
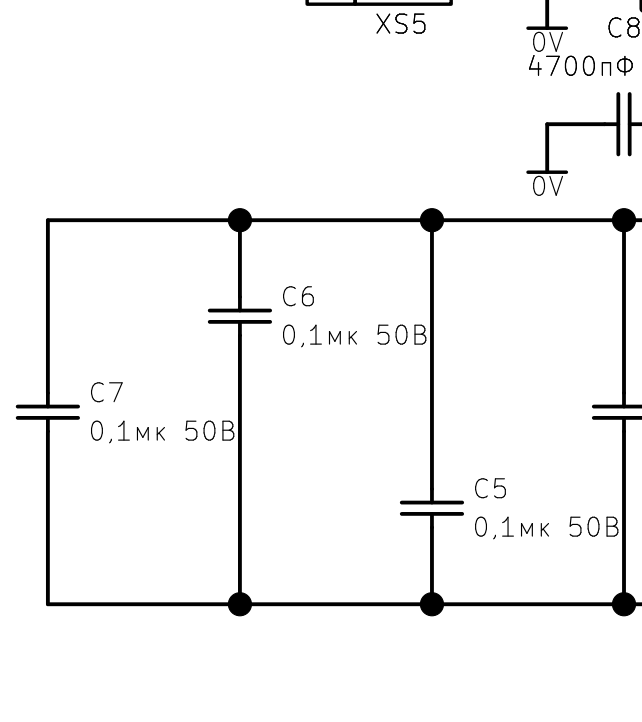
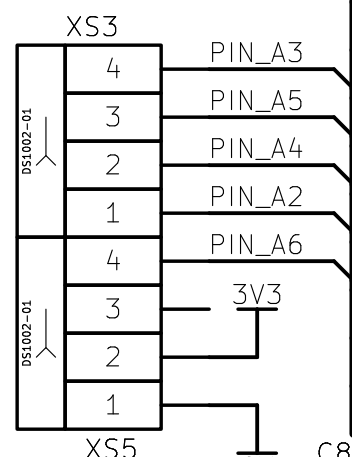


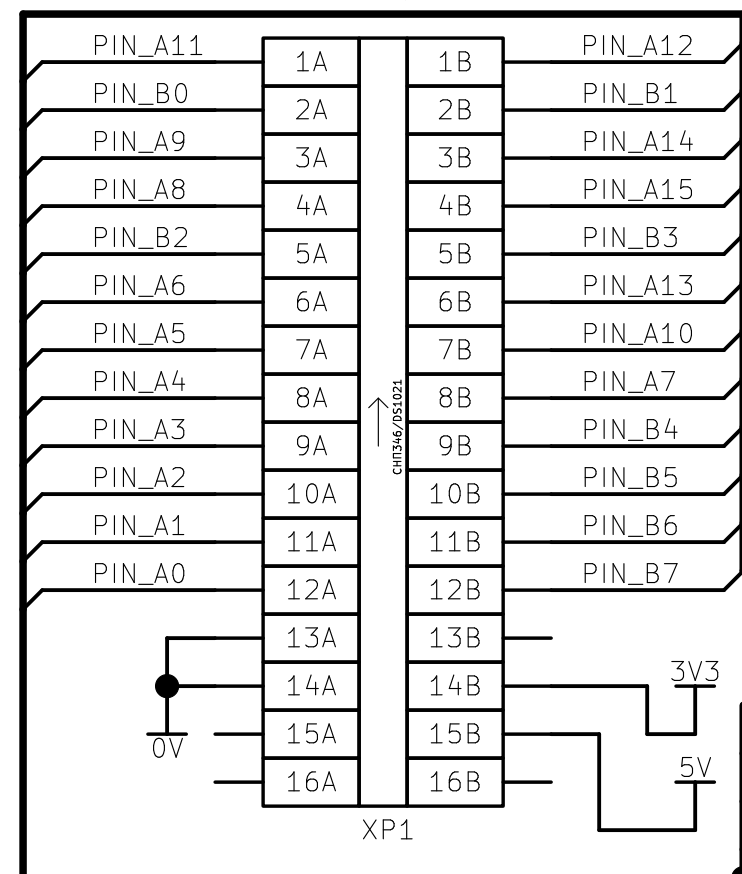

						ЭЗ			
Изм.	Лист	N докум.	Подп.	Дата		Лит.		Масса	Масштаб
Разраб.		Никитин Н.В.						-	-
Пров.									
Т.контр.						Лист		Листов 1	
Н.контр.									
Утв.									