

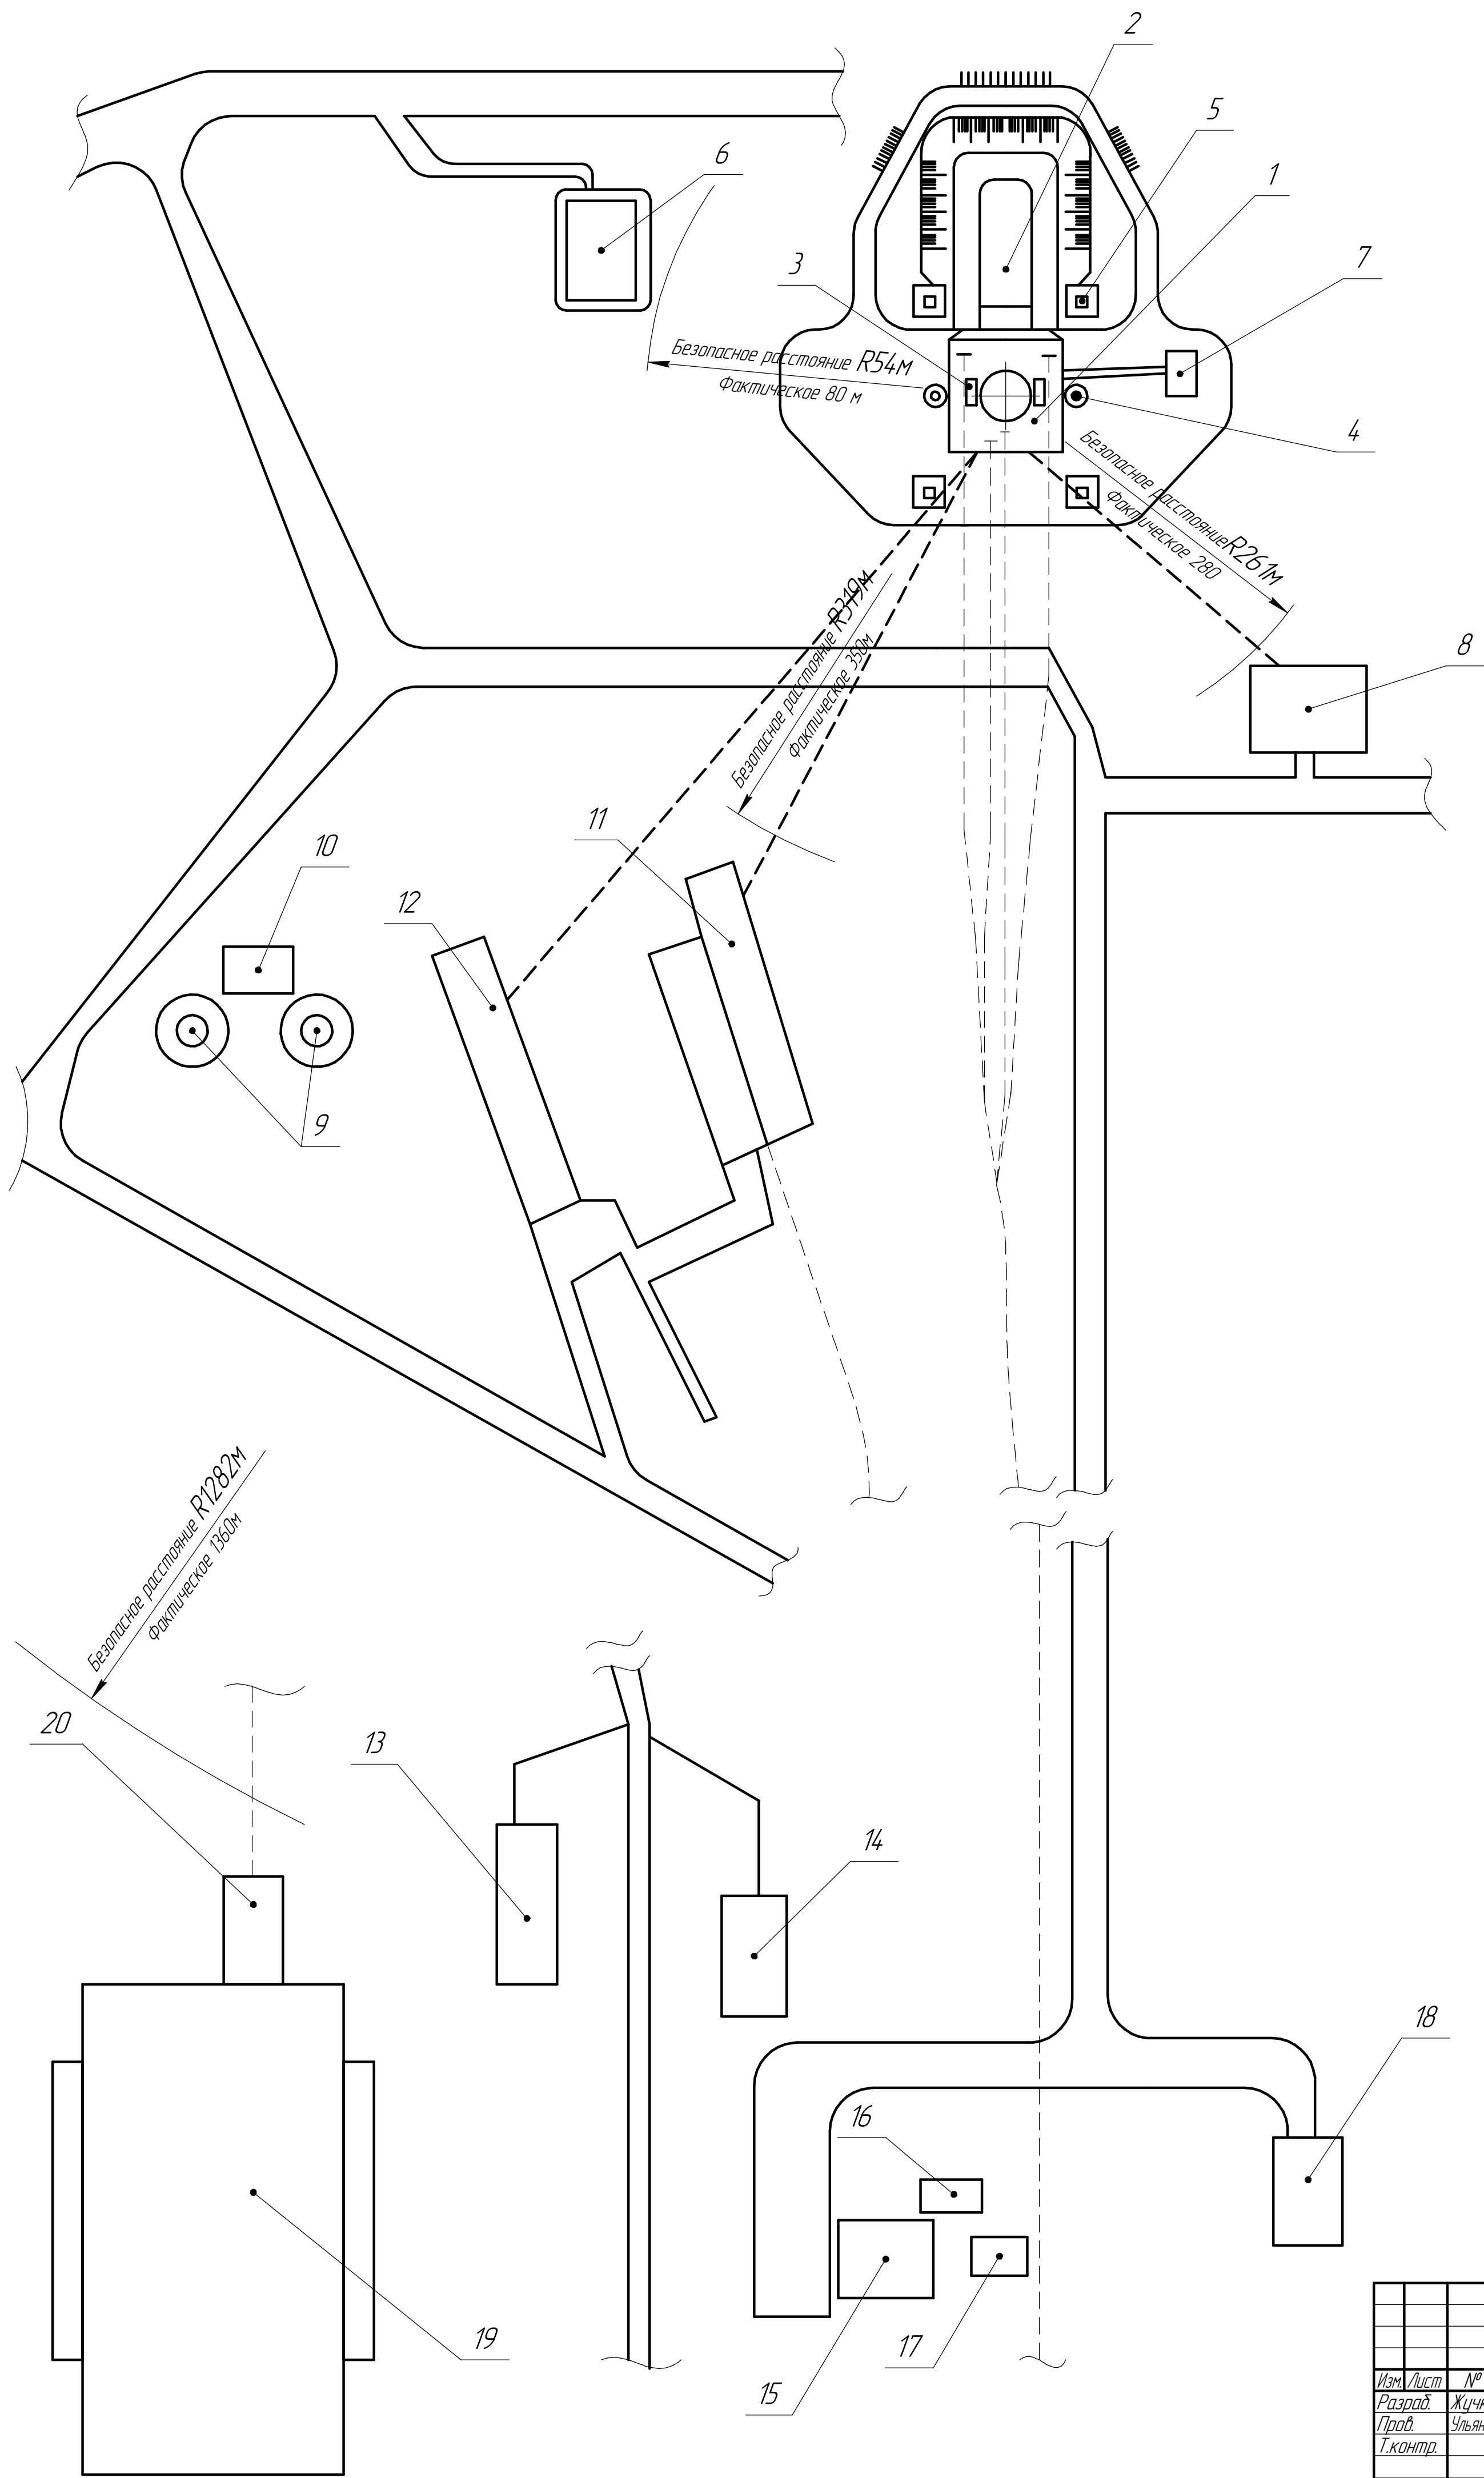
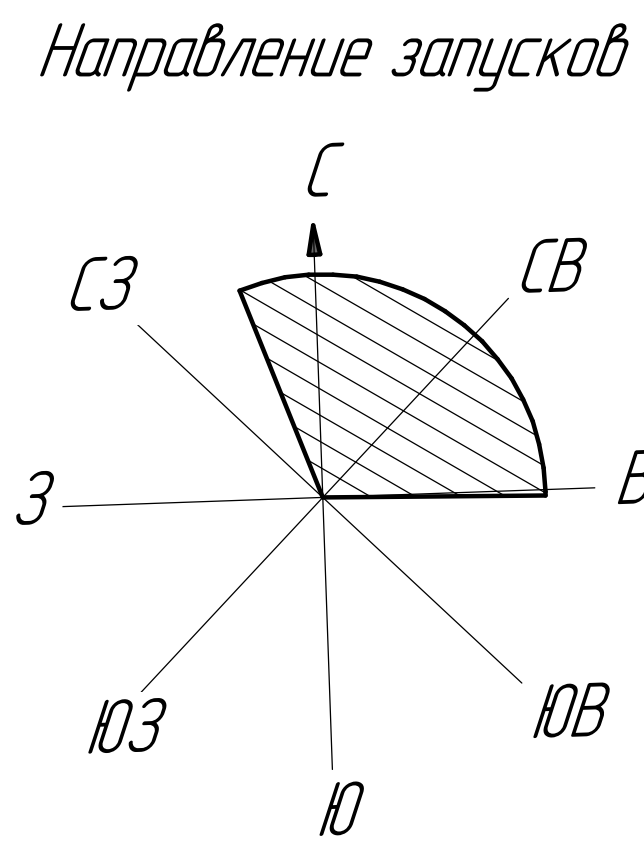


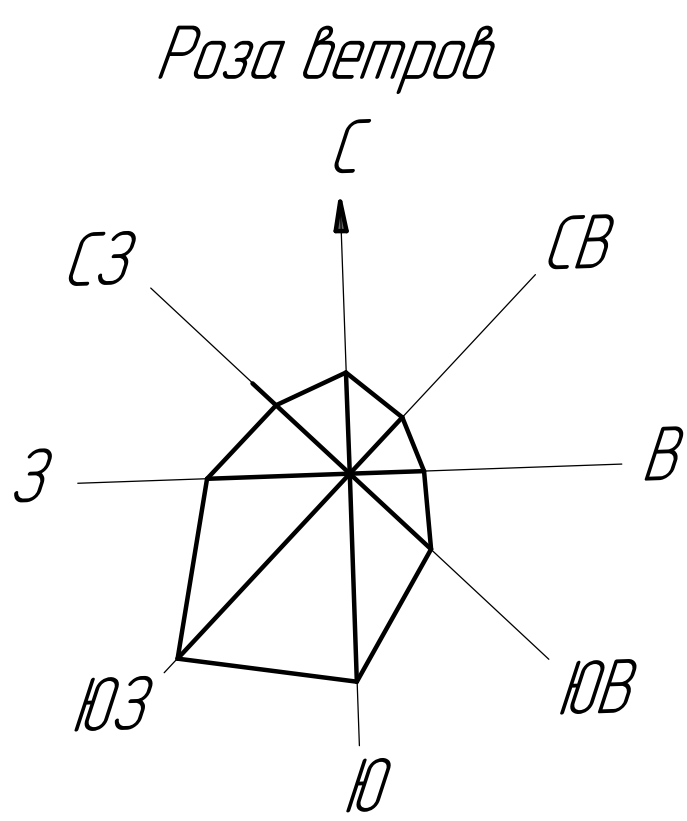

№	Наименование
1	Стартовое сооружение
2	Газоход
3	Ферма обслуживания
4	Башня дивертор
5	Прожекторная мачта
6	Командный пункт
7	Укрытие для персонала
8	Хранилище "Г"
9	Резервуары воды
10	Система пожаротушения
11	Хранилище "О"
12	Хранилище жидкого N2
13	Компрессорная станция
14	Хранилище РГ-1
15	Дизельная электростанция
16	Насосная станция
17	Элементы водоснабжения
18	Пункт охраны
19	МИК
20	Площадка обслуживания ТУА

Схема монтажно-испытательного корпуса

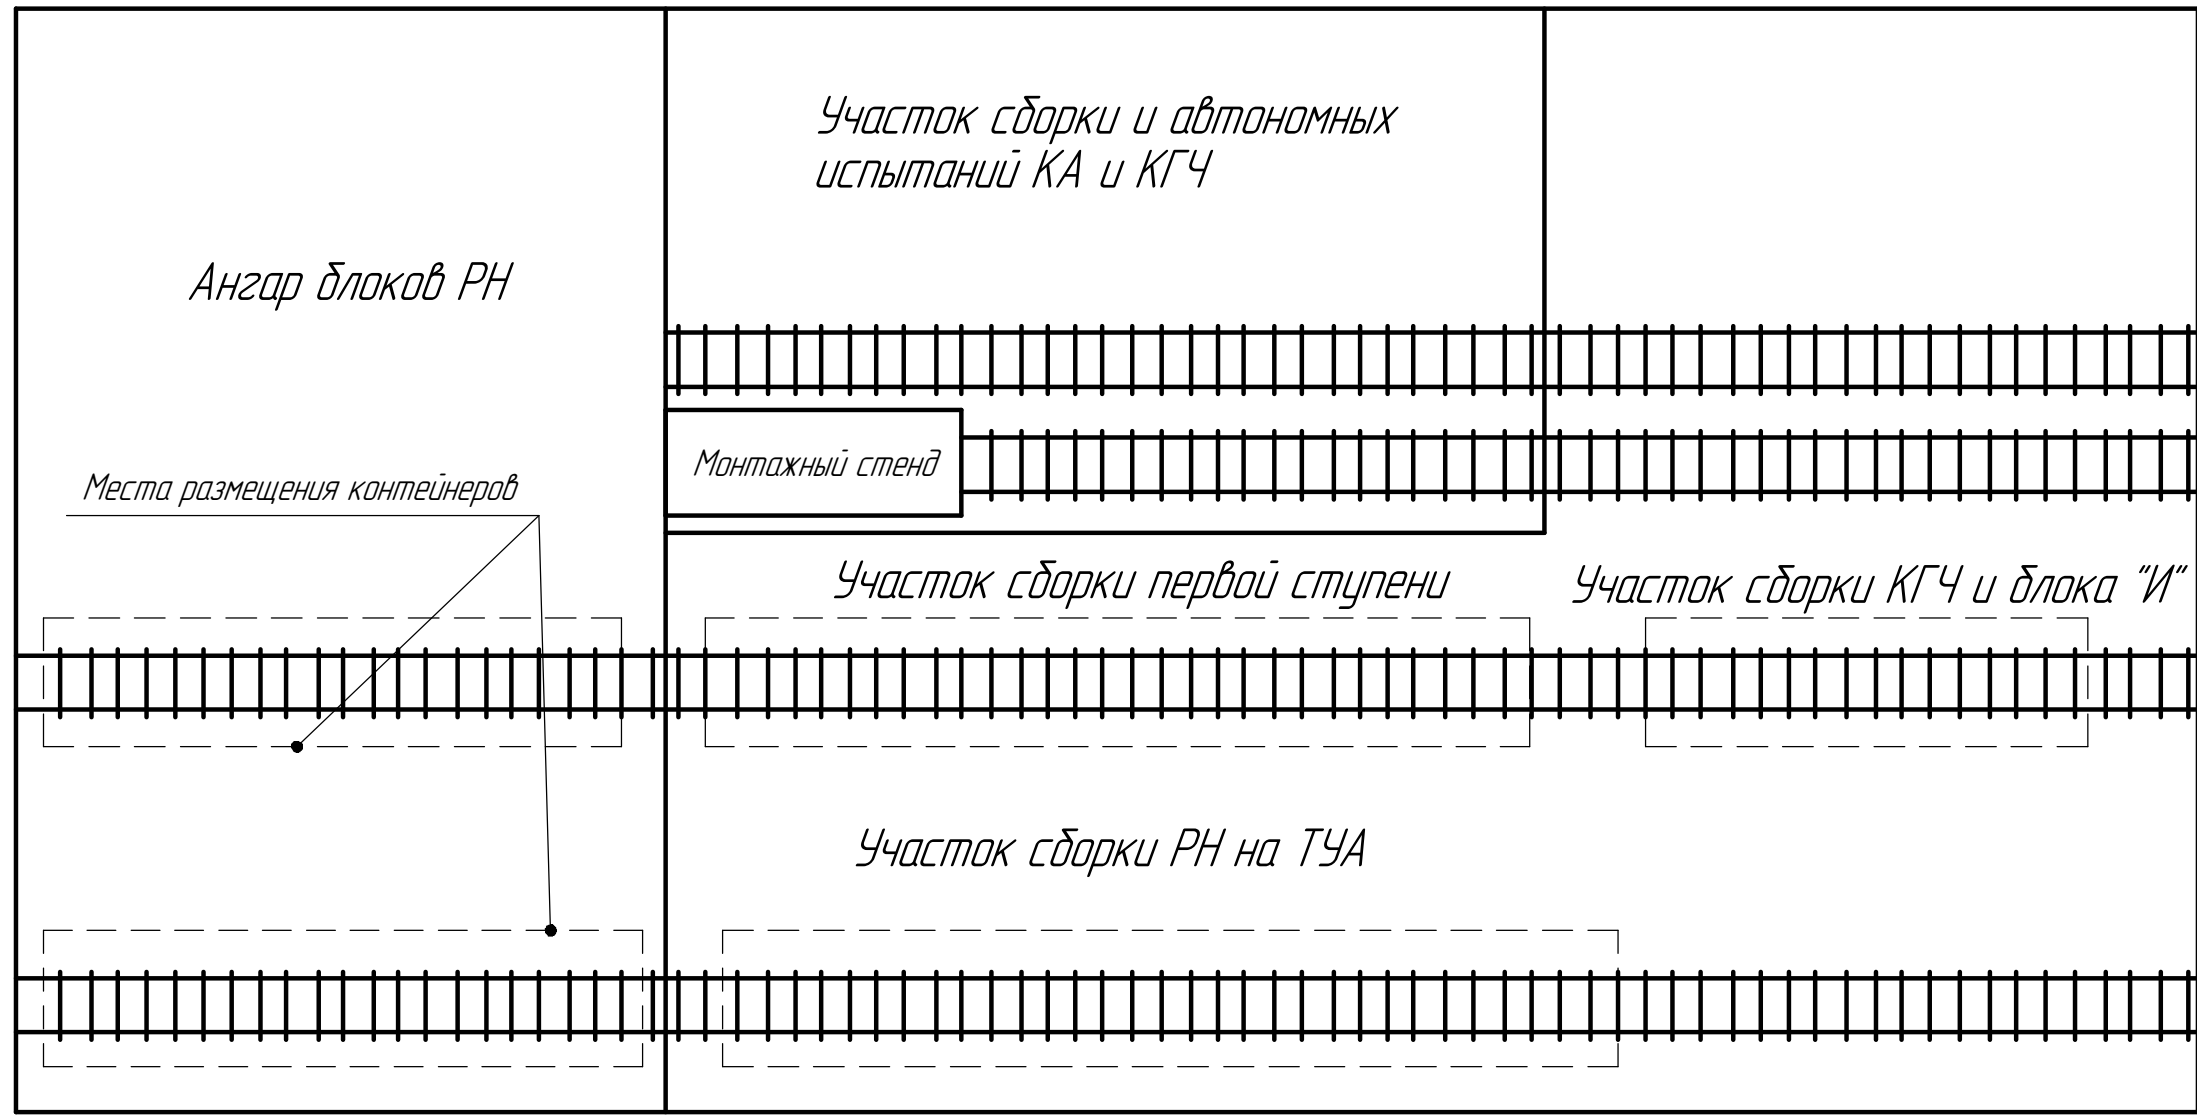

- Пути АД сообщения
- - - Пути ЖД сообщения
- - - - - Линии коммуникаций

Курсовой проект по НОРК									
Изм.	Лист	№ док.	Подп.	Дата	Генеральный план СК		Лист	Масштаб	Масштаб
Разраб.	Жуков П.А.	Жуков П.А.	Жуков П.А.	Жуков П.А.			1	1:2000	1:2000
Проб.	Ульянов А.В.	Ульянов А.В.	Ульянов А.В.	Ульянов А.В.	МГТУ им. Н.Э. Баумана		Лист	Листов	1
Т.контр.							МГТУ им. Н.Э. Баумана	группа	ПС4-102
Н.контр.					Копирован		Формат	А1	А1
Утв.									